PLAN DU REZ-DE-CHAUSSÉE

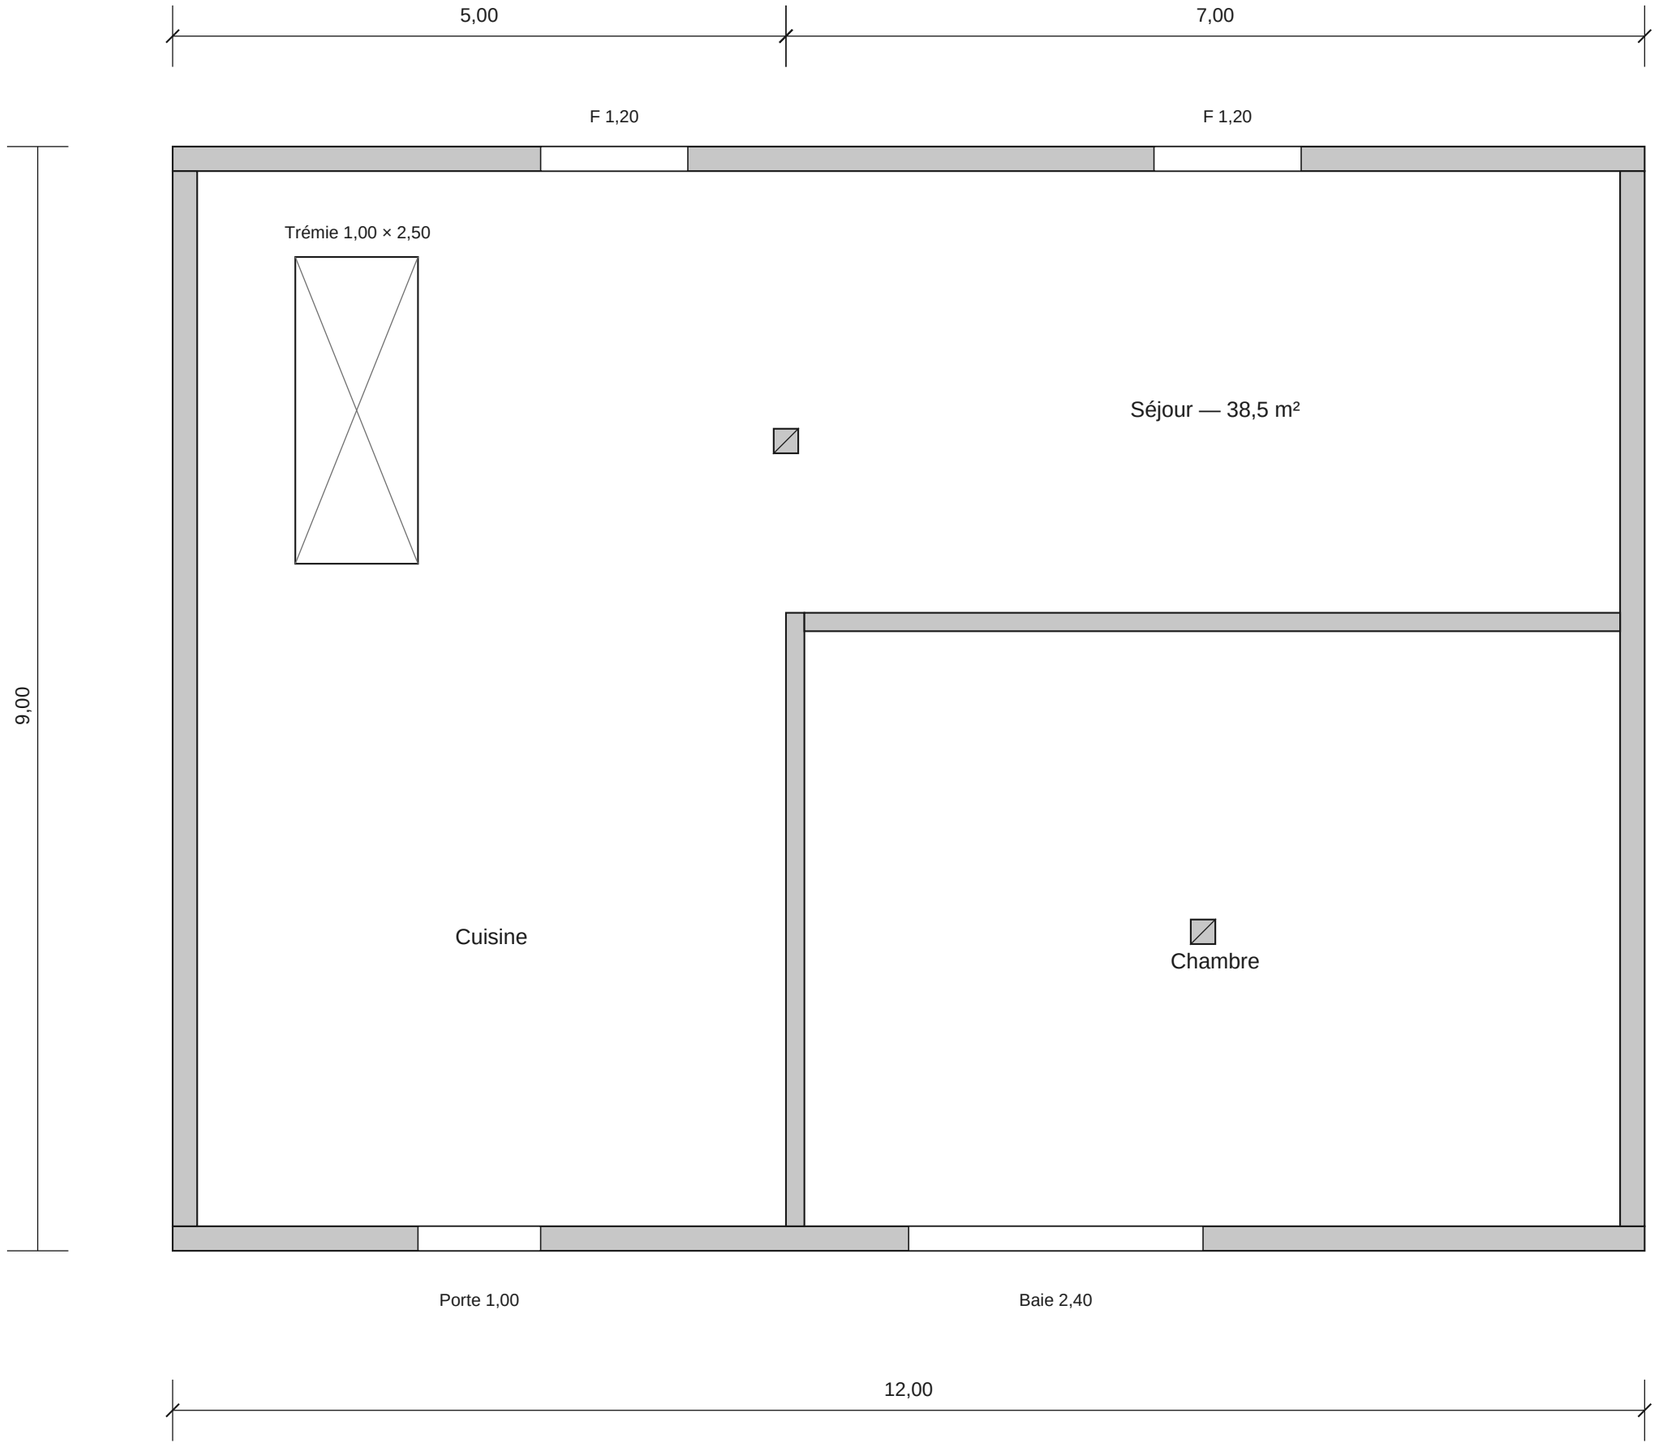

Voiles ext. ép. 20 cm, voiles int. ép. 15 cm, hauteur sous plafond 2,70 m. Plancher haut ép. 20 cm.
Cotes en mètres, nus bruts de béton.

PLAN DE DÉMONSTRATION — FICTIF

Résidence Les Tilleuls — maison type T4
RDC — Plan de structure
Échelle 1/50 — Format A3

Document sans valeur contractuelle — Métré BA

PLAN DE FONDATIONS

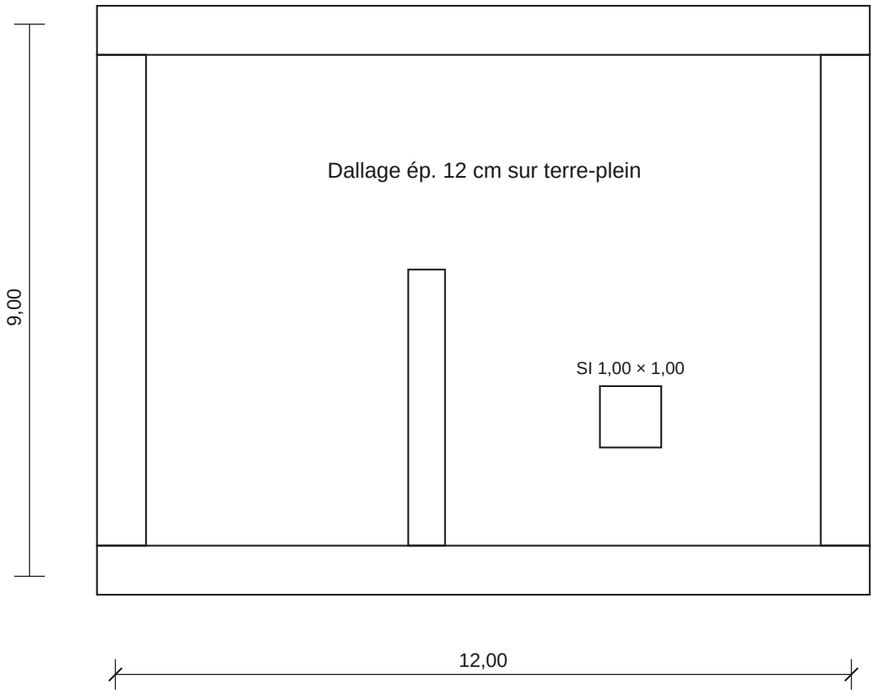

Semelles filantes ext. 0,80 × 0,40, int. 0,60 × 0,40. Semelles isolées 1,00 × 1,00 × 0,40.
Cotes en mètres, nus bruts de béton.

PLAN DE DÉMONSTRATION — FICTIF

Résidence Les Tilleuls — maison type T4
Fondations — Semelles et dallage
Échelle 1/100 — Format A3

Document sans valeur contractuelle — Métré BA